


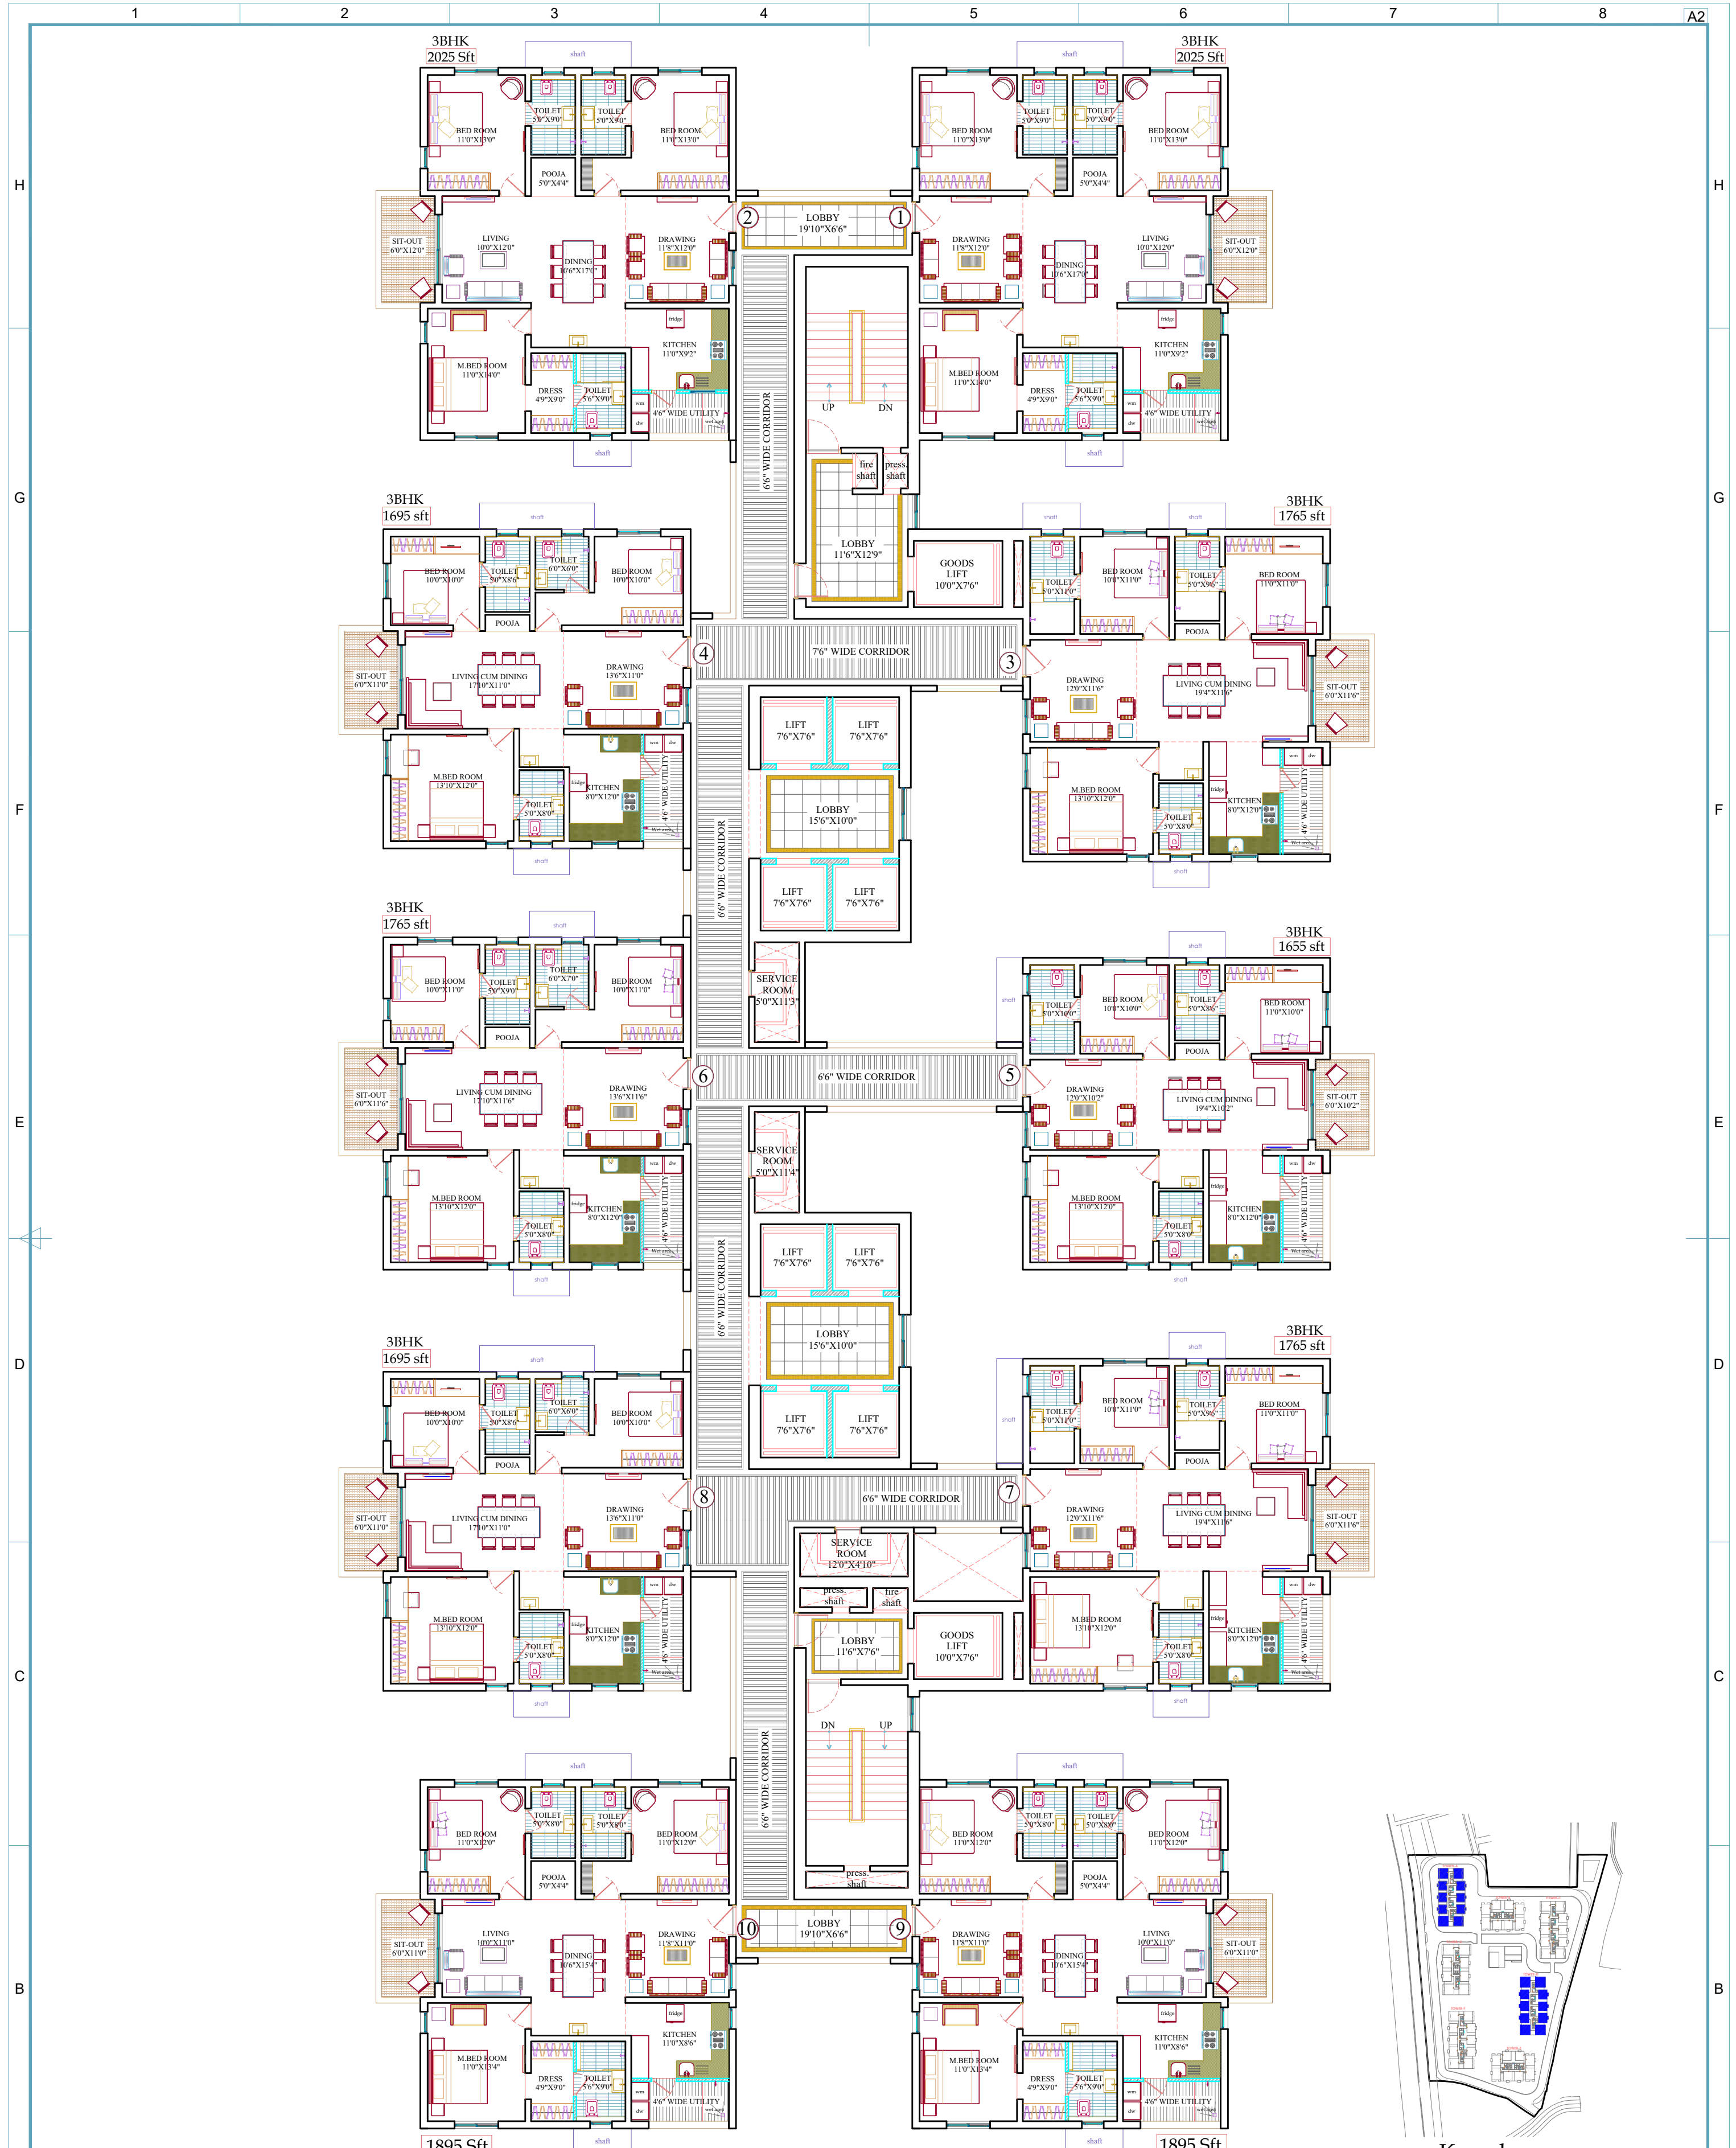

Key plan

OPTION-2 (Center balcony)

Title Typical floor plan-TOWER-A&D			Client M/S. TEAM4 LIFE SPACES.				Architects  Genesis Planners Pvt. Ltd Laxmi Towers, Plot No.559, Road No.92, Jubilee Hills, Hyderabad, India-500033 Ph:040-66977777 Fax:040-23555549 email - info@genesisplanners.in website - www.genesisplanners.in	
Date 02-04-2025	Dwg No. GP-2354-SD-AD-A1-05		Project / Location PROPOSED RESIDENTIAL APARTMENTS @ MIYAPUR, HYD.		North			
Dealt KMJ	Architect GVL	Rev No. 00	General Note : All dimensions are in millimeters unless otherwise specified, and do not scale this drawing, only written dimensions are to be followed.		M/s. G E N E S I S P L A N N E R S Pvt. Ltd. HAS THE COPY RIGHTS OF THIS DOCUMENT, AND IT SHOULDN'T BE USED BY ANYBODY WITHOUT THE WRITTEN PERMISSION OF THE CHIEF ARCHITECT.		vision > transform	